


Übersichtsschema Energiemessungen

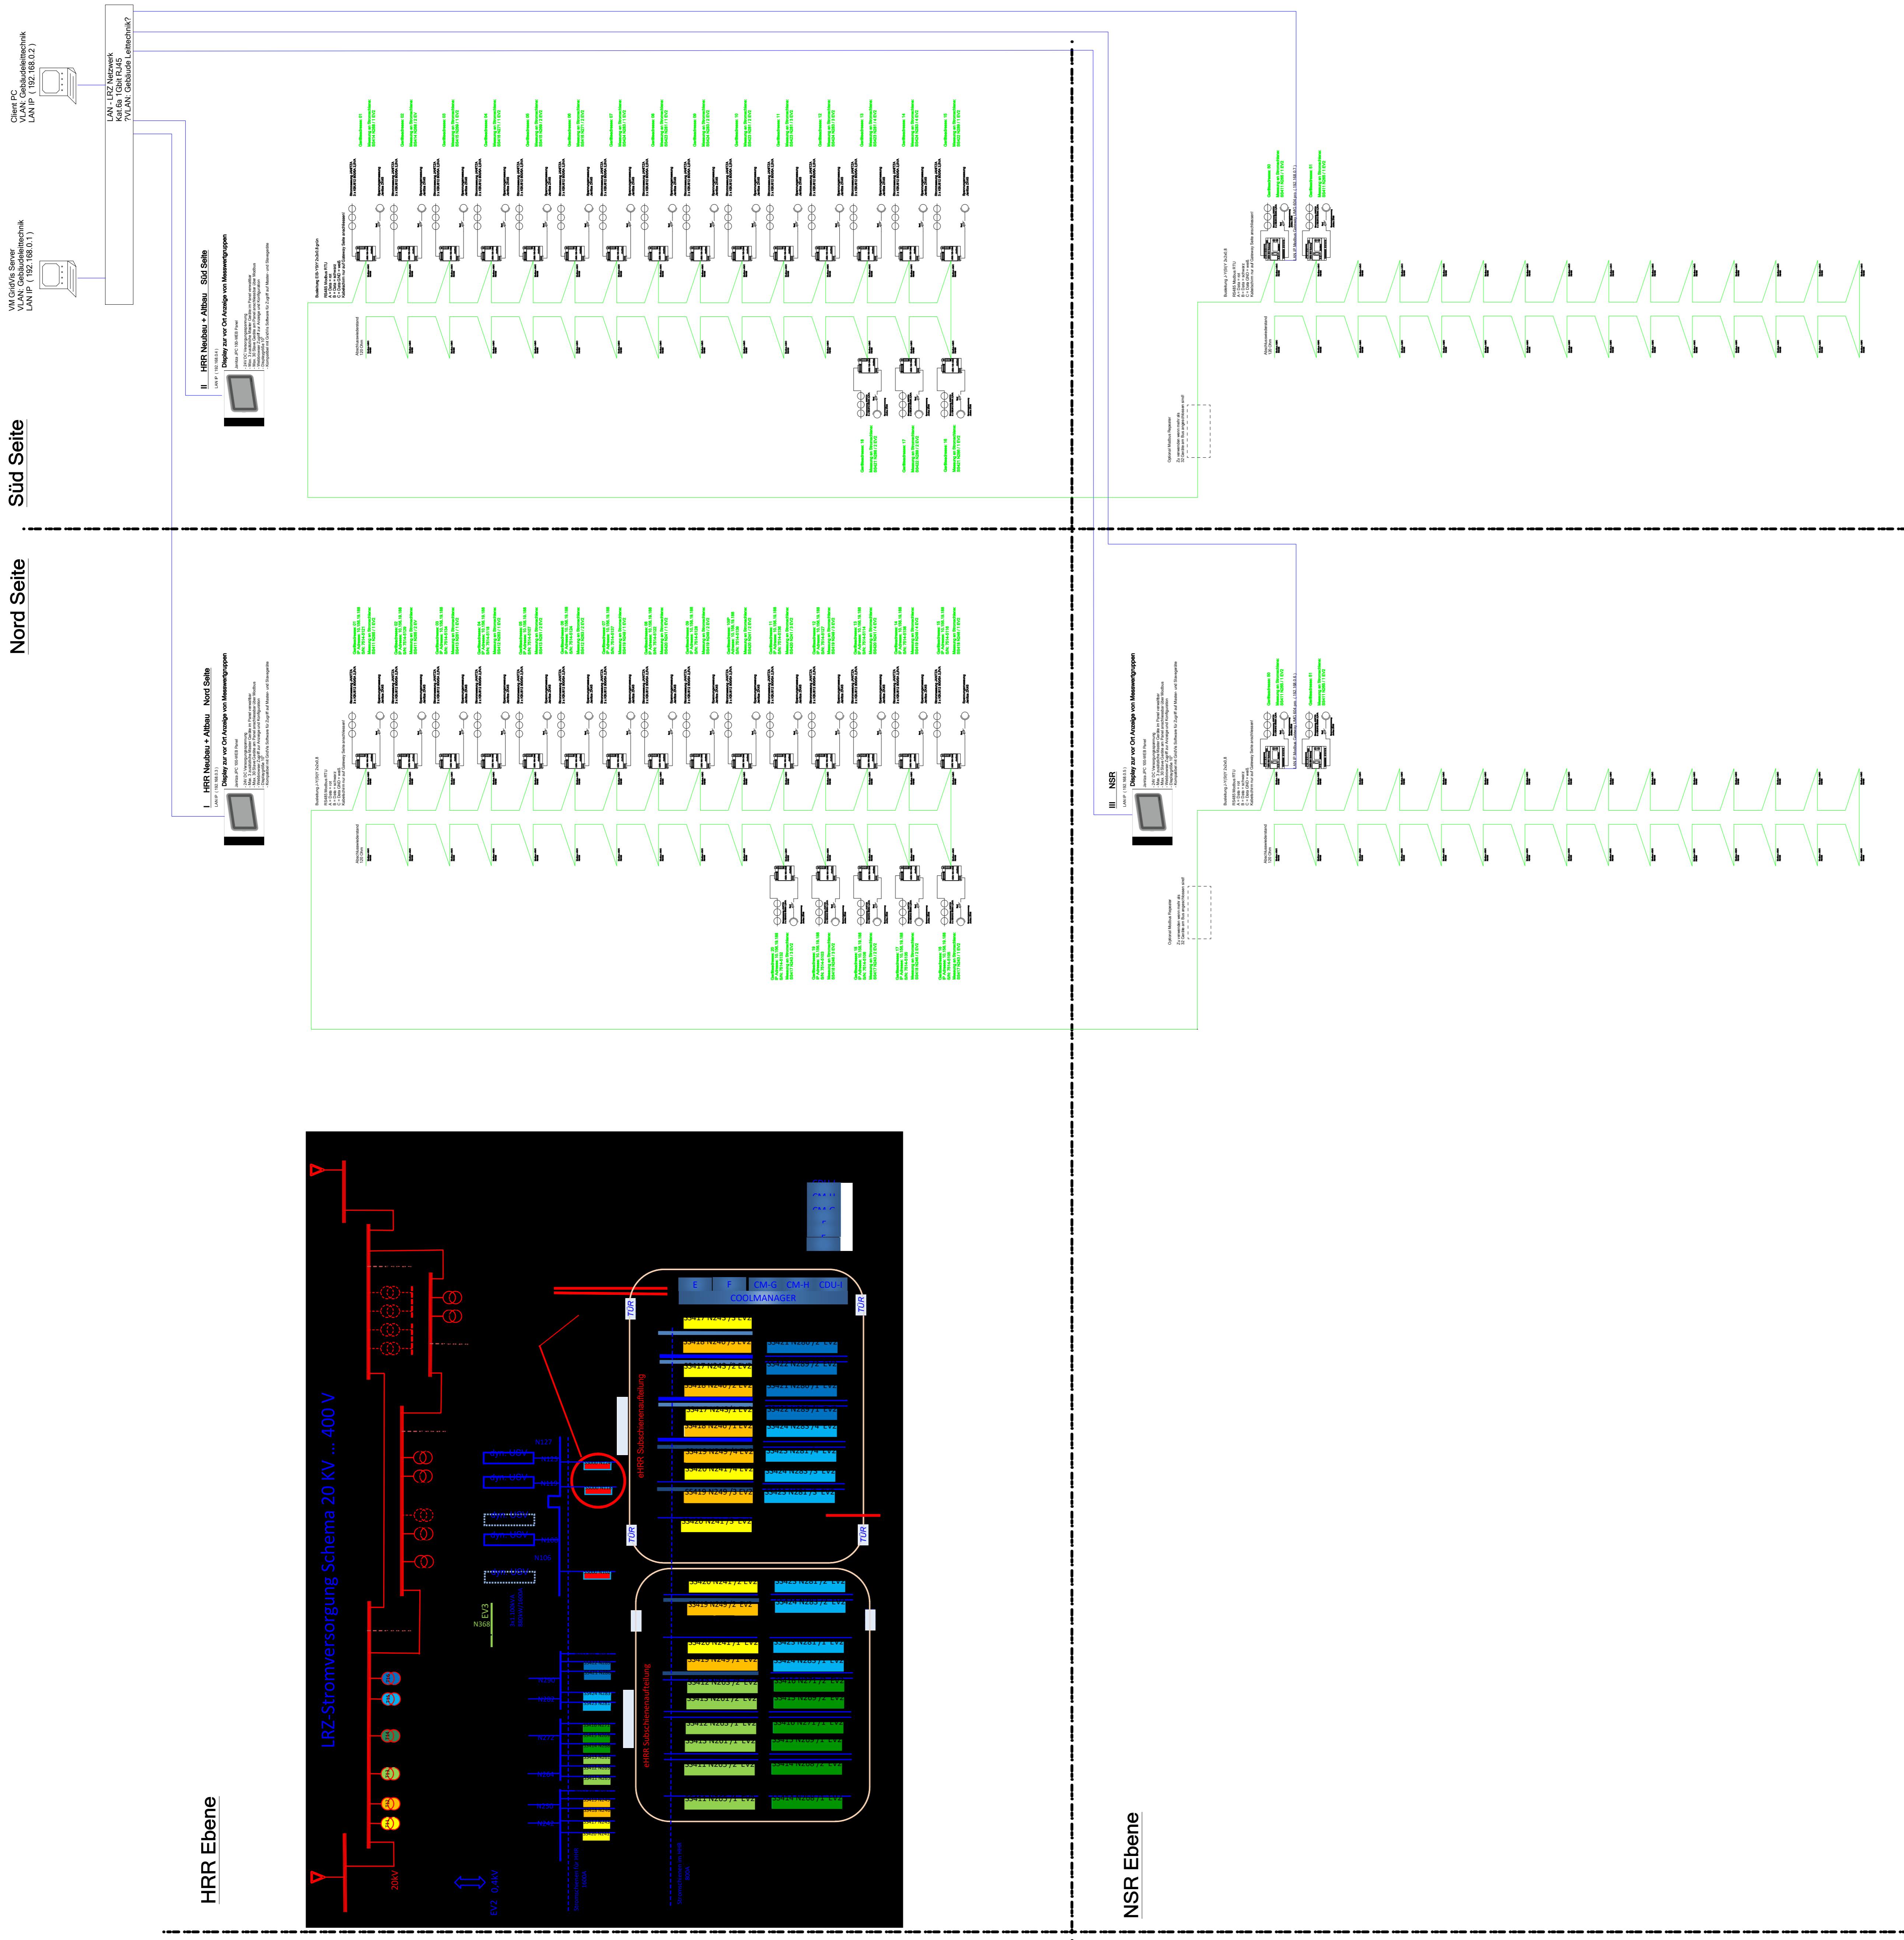

DAR Ebene

Auftraggeber		Bauvorhaben	
LRZ		Leibniz-Rechenzentrum Boltzmannstraße 1 D-85748 Garching	
Zeichnung:		Projekt: P180043-397 LRZ Energieremessung	
Blatt:	Größe:	Datei:	Index
		P181900	Änderungen
Stand:	Name:		Index
Basis:	Datum:		Änderungen
Grp.:	11.01.2023		Index
		geändert am	
		geändert von	

elektro
SCHATTENKIRCHNER

Maßstab:	1:100
----------	-------